

EY

EIWEN CF YING PORTFOLIO - 2026



Arkitekt MAA · Concept Lead

Arkitekt med over 10 års erfaring i tidligfase-design, konceptudvikling og arkitektonisk ledelse inden for byudvikling, transformation og byggeri.

Jeg arbejder med at omsætte komplekse steder, projektbriefs og interessenlandskaber til klare, stedforankrede arkitektoniske hovedgreb – *og med at fastholde disse gennem myndighedsdialog, tværfaglig koordinering og videre projektering.*

Min styrke ligger i at skabe struktur i kompleksitet og definere koncepter, der kan bære både fagligt, rumligt og strategisk.

Jeg bevæger mig fleksibelt mellem **arkitektonisk ophav i de tidlige faser** og designansvar i efterfølgende processer, afhængigt af projektets karakter og organisering.

Arkitektur opstår, når klarhed får form.

- Stedslighed og kontekstuelle hovedgreb
- Tidlige studier, feasibility og strategisk rammesætning
- Rumlige sekvenser og narrativ formgivning
- Materialitet, taktilitet og lys som bærende arkitektoniske drivere
- Fastholdelse af designintention i komplekse samarbejder
- Udvikling og anvendelse af nye arkitektoniske værktøjer i designprocessen



**EIWEN CF
YING**

Arkitekt MAA · Concept Lead

Aarhus C
ey.nordic@gmail.com
+45 4243 6600
www.linkedin.com/in/eiwenying



Østre Søbad - Silkeborg · 2017



KK Wind Fitness Pavilion - Ikast · 2024



JAKA Seniorbofællesskab - Aarhus · 2025



Papirtårnet - Silkeborg · 2017



Jern og Metal Skole - Sisimiut · 2025

Udvalgte projekter inden for byudvikling, transformation, offentlige bygninger og tidligfase.




Jeg arbejder som konceptuel arkitekt i krydsfeltet mellem tidligfase, strategisk rammesætning og designledelse.

Min rolle er at skabe klarhed i komplekse projekter – at formulere et stedforankret hovedgreb, etablere en fælles arkitektonisk retning og sikre, at designintentionen kan bæres videre gennem myndighedsdialog, koordinering og realisering.

Jeg påtager mig ansvar i de tidlige faser, hvor retning fastlægges, og arbejder videre som sagsarkitekt eller designansvarlig, når projektet kræver kontinuitet.

VÆRDIGT

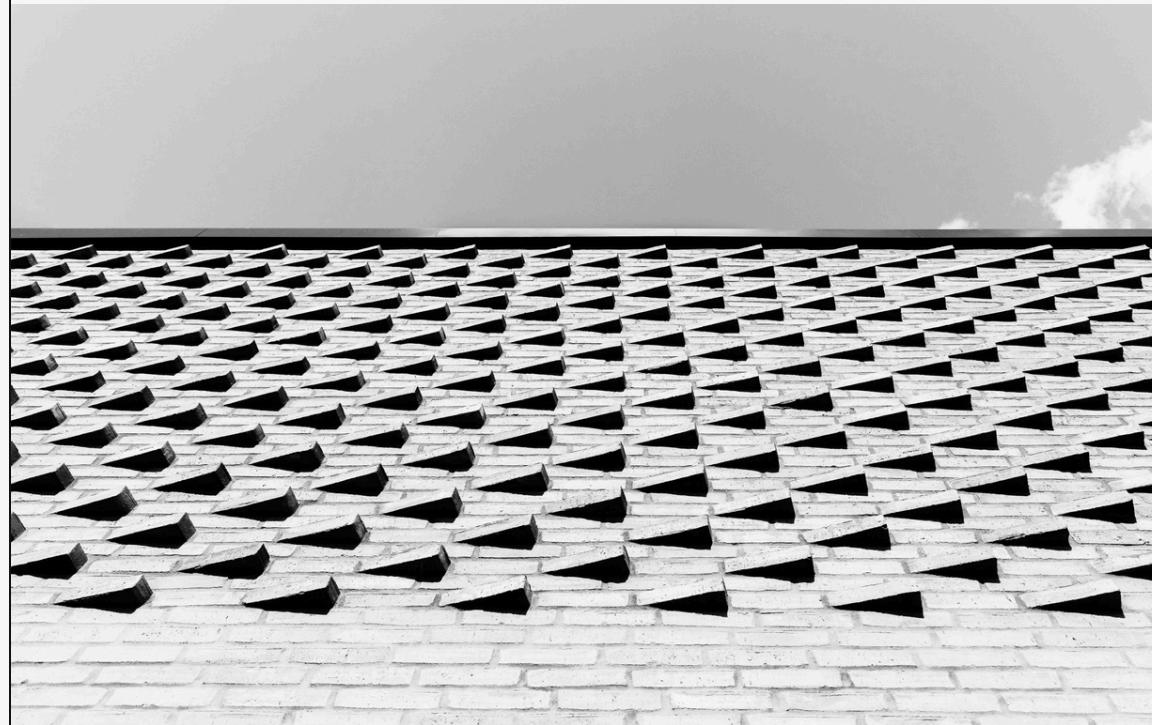

Arkitektur skal udvise respekt for mennesker, steder og sammenhænge.

Jeg arbejder med proportion, materialitet og rumlig ro som grundlag for arkitektonisk værdighed – uafhængigt af skala og program.

POETISK



Poetik opstår, når funktion, rum og lys samles i klare sekvenser.

Jeg arbejder bevidst med bevægelse, overgange og sanselige kvaliteter, så arkitekturen kan opleves – ikke forklares.

FORANKRET



Ethvert projekt udspringer af sit sted.

Kontekst, topografi, eksisterende strukturer og brugsmønstre er aktive drivere i mit arbejde og danner grundlag for robuste, stedbundne løsninger.





Jern- og Metalskole, Sisimiut

Rolle:


Konceptansvarlig – arkitektur, stedstrategi og rumlig organisation
(Modellering og tegningsgrundlag; visualisering i tæt sparring)

Skolen placeres som et forbindende led mellem eksisterende uddannelser, by og landskab
Bevægelsesmønstre (hverdag og sæson) informerer bygningens form og orientering
Arkitekturen forstås som en del af byens infrastruktur frem for et isoleret objekt.

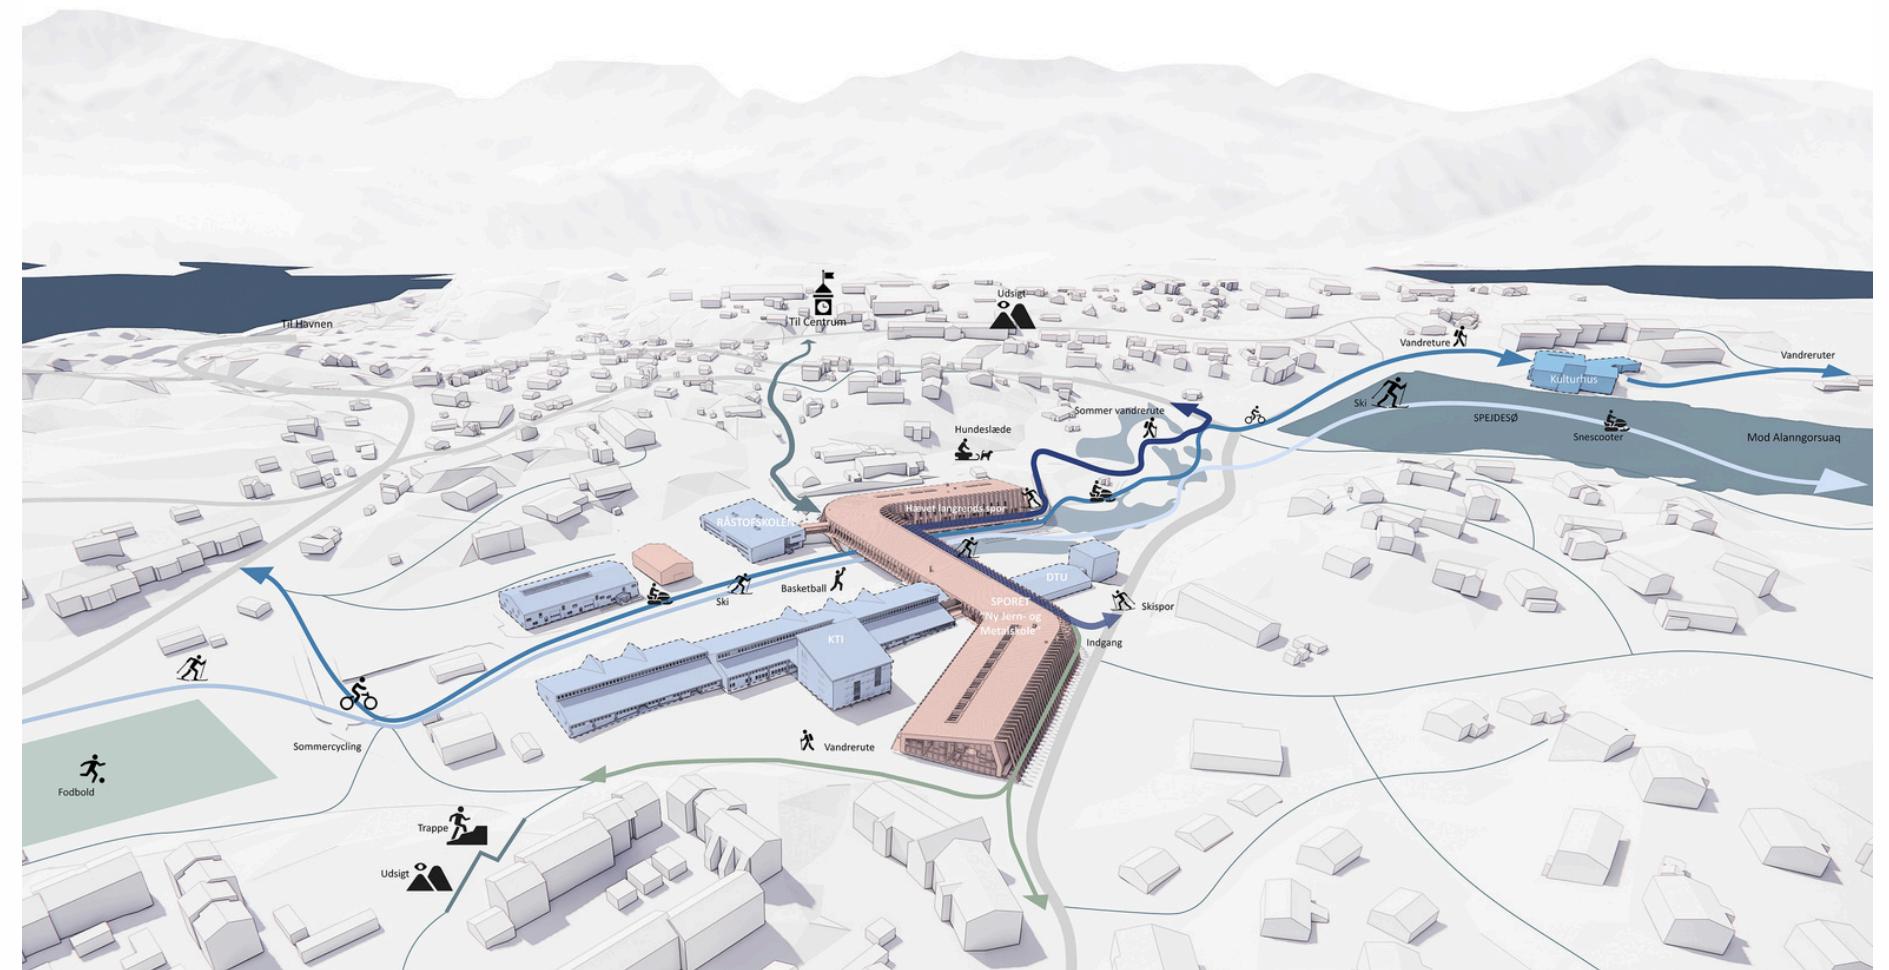


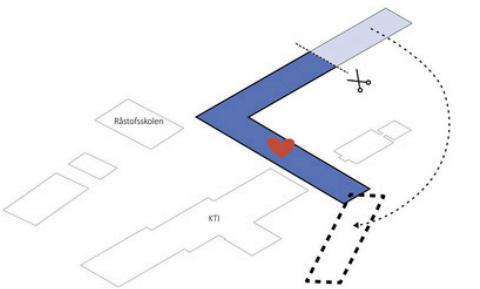


HOVEDGREB - En bygning der forbinder KTI og Råstofskolen henover den grønne kile, med alle værksteder og undervisningsrum placeret på nordsiden, bliver meget langt, og med langt til fællesarealerne. Ved at omidisponere ideoplæget og placere noget af skolen på det flade areal mod syd, bliver der tilgængeligt adgang til fællesarealerne for alle uddamsele.


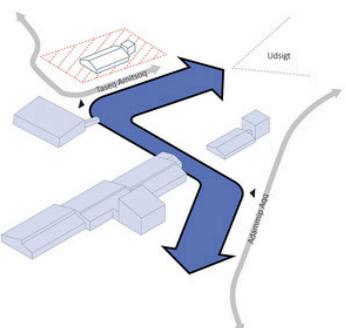



EN BYGNING, EN BRO, EN FORBINDELSE - Den nye skole optager retningerne i landskabet og skaber nye forbindelser i byen. Den peger mod den smukke udsigt i mod Spejdfjord.

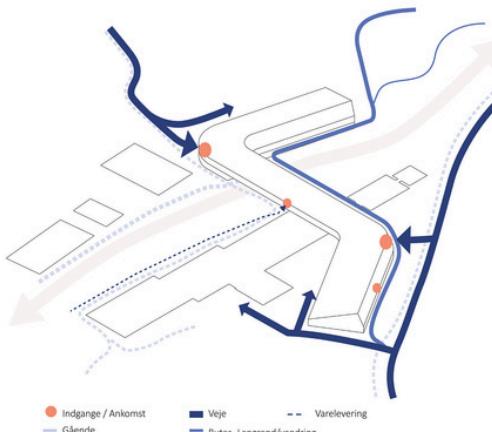

● Indpange / Ankomst
— Gående
— Veje
— Varelevering
— Ruter- Langrend/Vandring

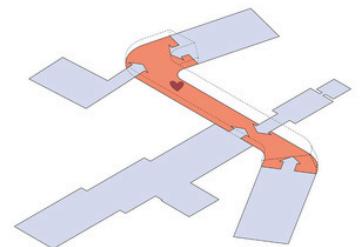

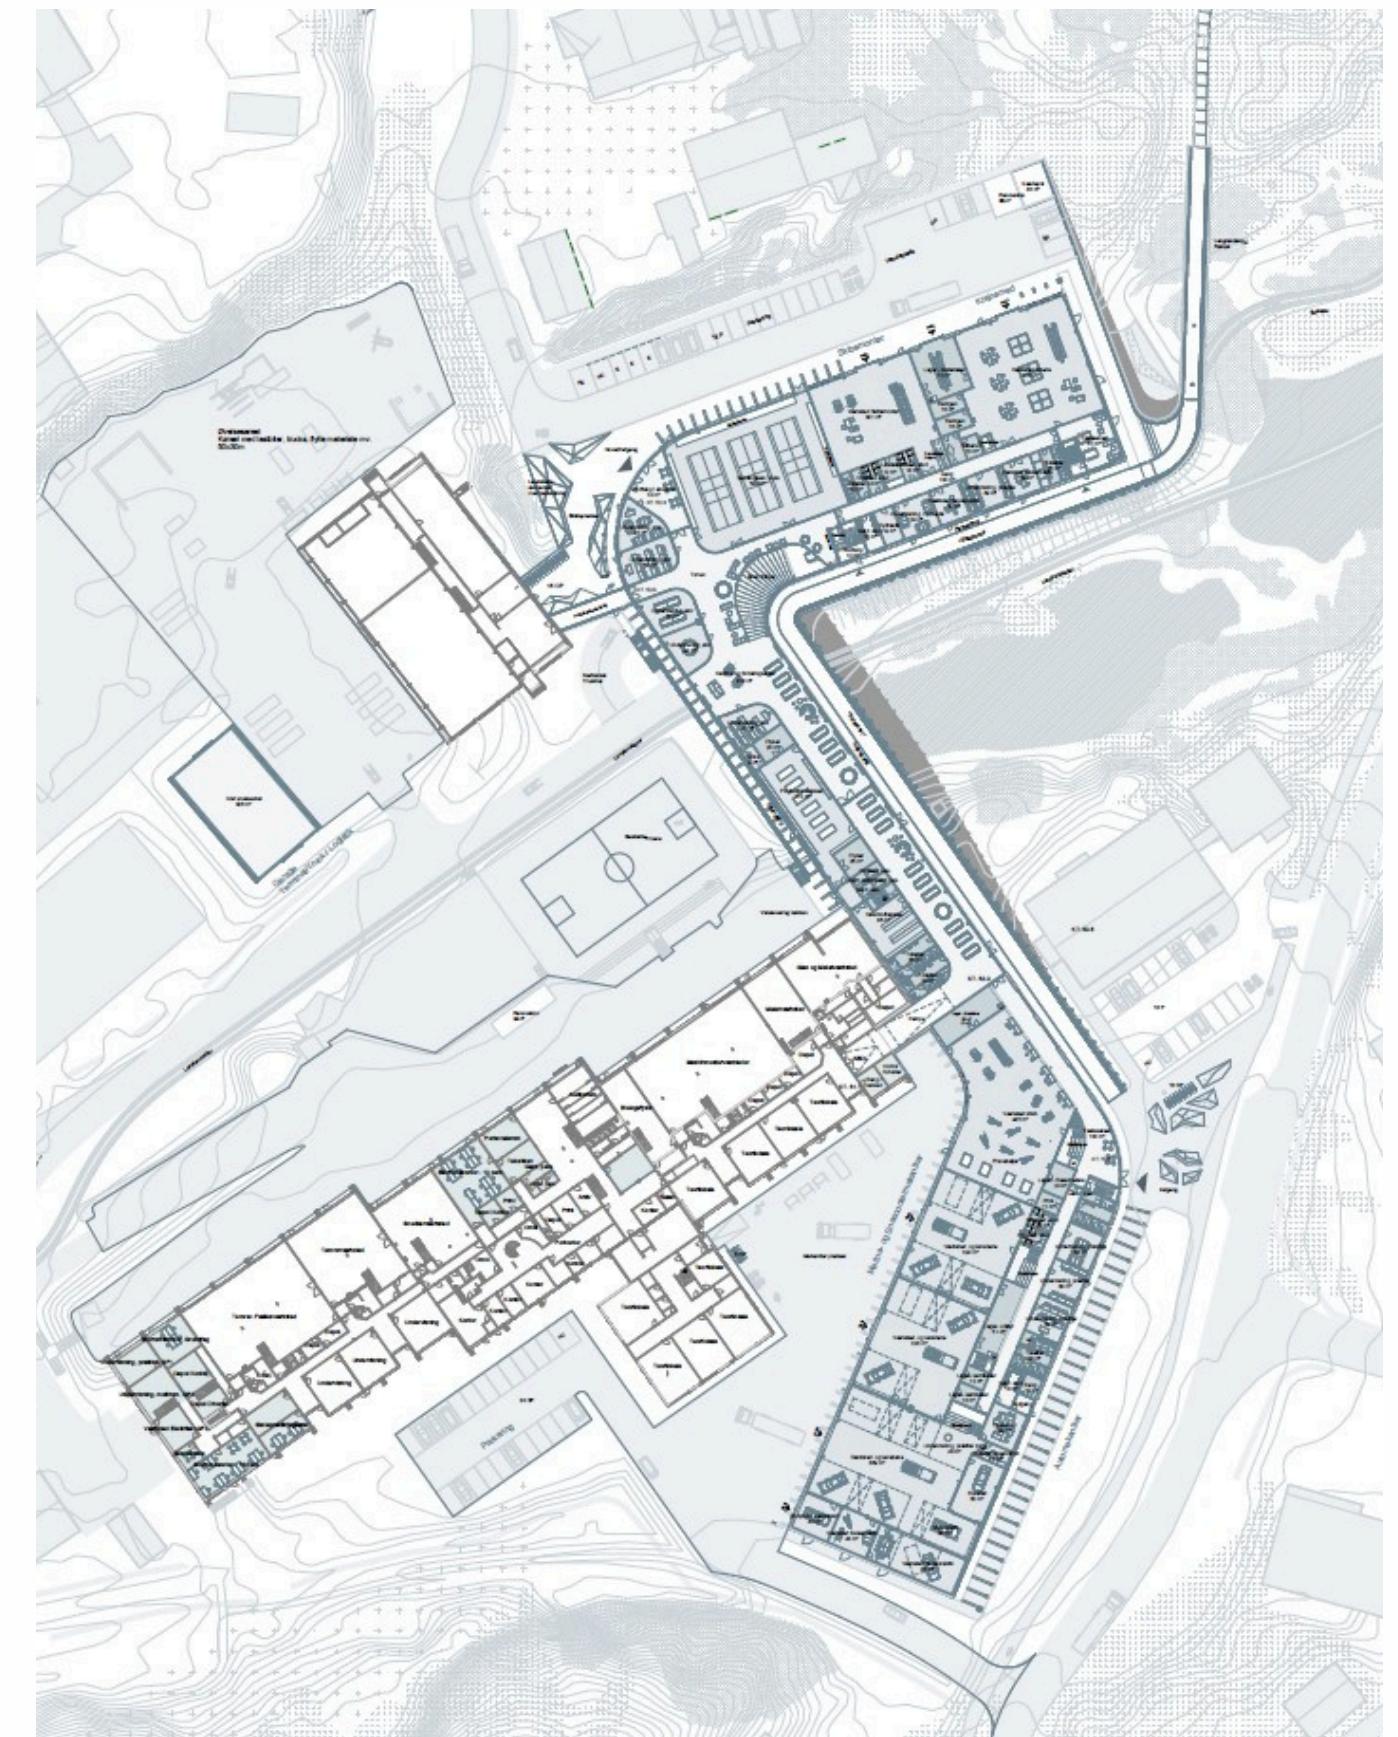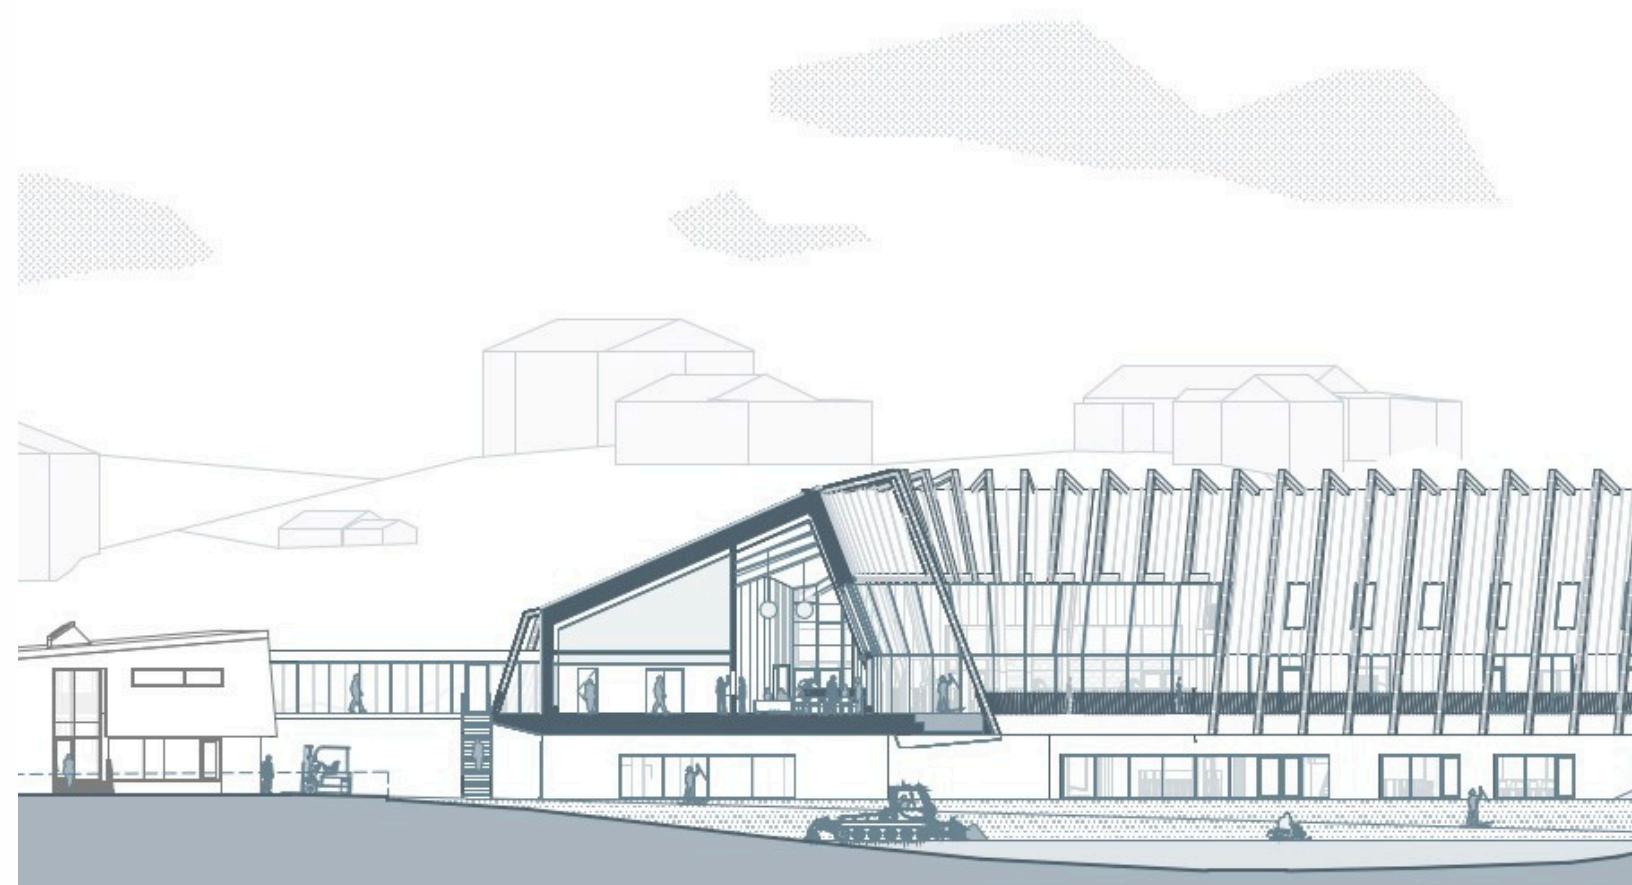

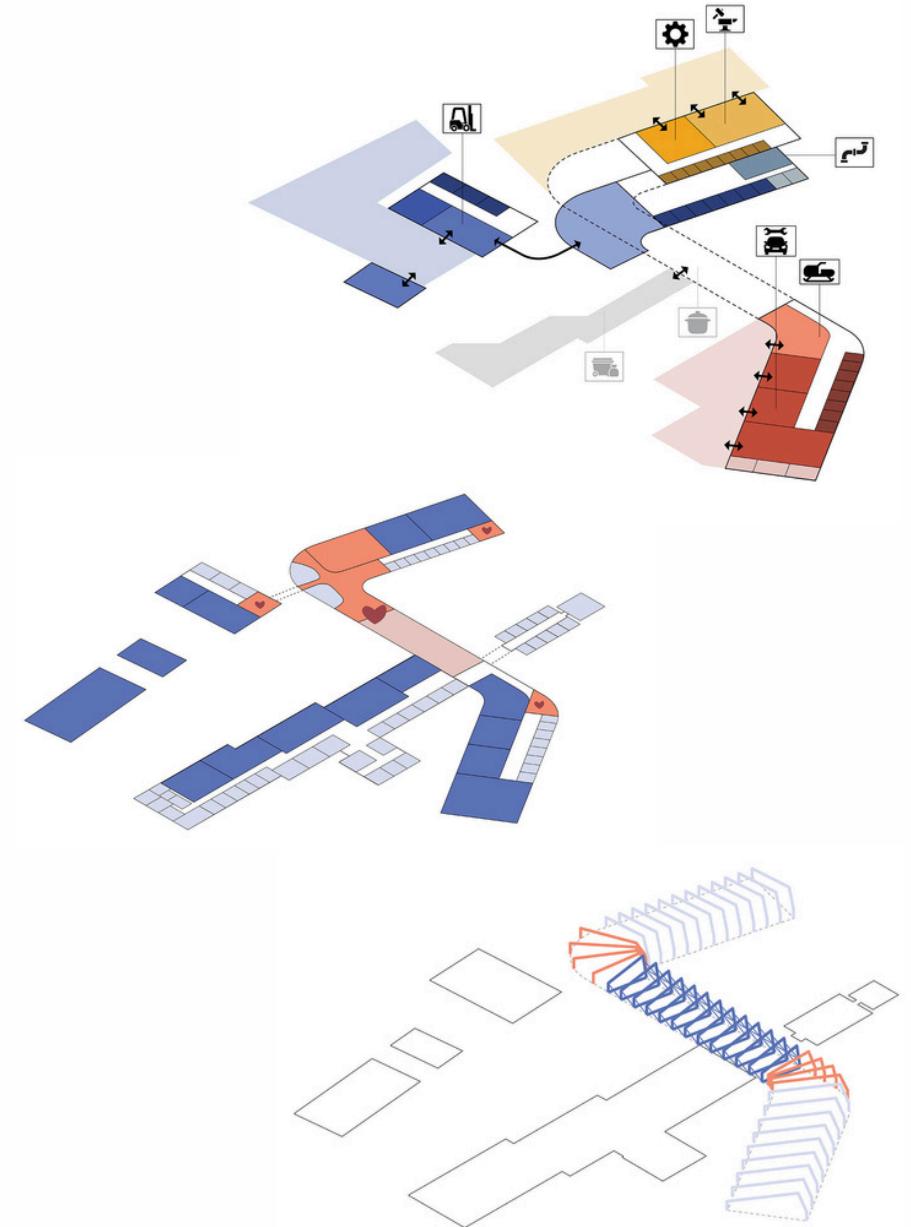

SPORET

Et spor tegnes i sneen.
Melle m fjeld og fjord,
mellem hånd og tanke,
mellem menneske og sted.

Her mødes by og landskab,
uddannelse og liv.
Spor flettes, krydses, fortsætter
- hver retning en mulighed.

Som skiene i sneen
trækker vi linjer,
forbinde,
former vejen videre.
et spor i livet.






KK Windsolutions, Ikast



Løbende arkitektoniske opgaver

Rolle:


Konceptudvikling og arkitektonisk rådgivning for KK Wind Solutions under rammeaftale. Sagsansvarlig arkitekt og primær kontaktperson med ansvar for flere arkitektoniske delprojekter på virksomhedens campus, herunder fitnesspavillon, transformation og optimering af eksisterende fabriksbygning til kontormiljø, etablering af cykel-parkering, samt overordnede disponerings- og oversigtsstudier.

Arbejdet omfattede formgivning, rumlig disponering, materialestrategi samt budgetudarbejdelse og dialog med træleverandører. Projektet er igangværende og udføres i tæt samarbejde med bygherre med fokus på kvalitet, økonomi og arkitektonisk sammenhæng.

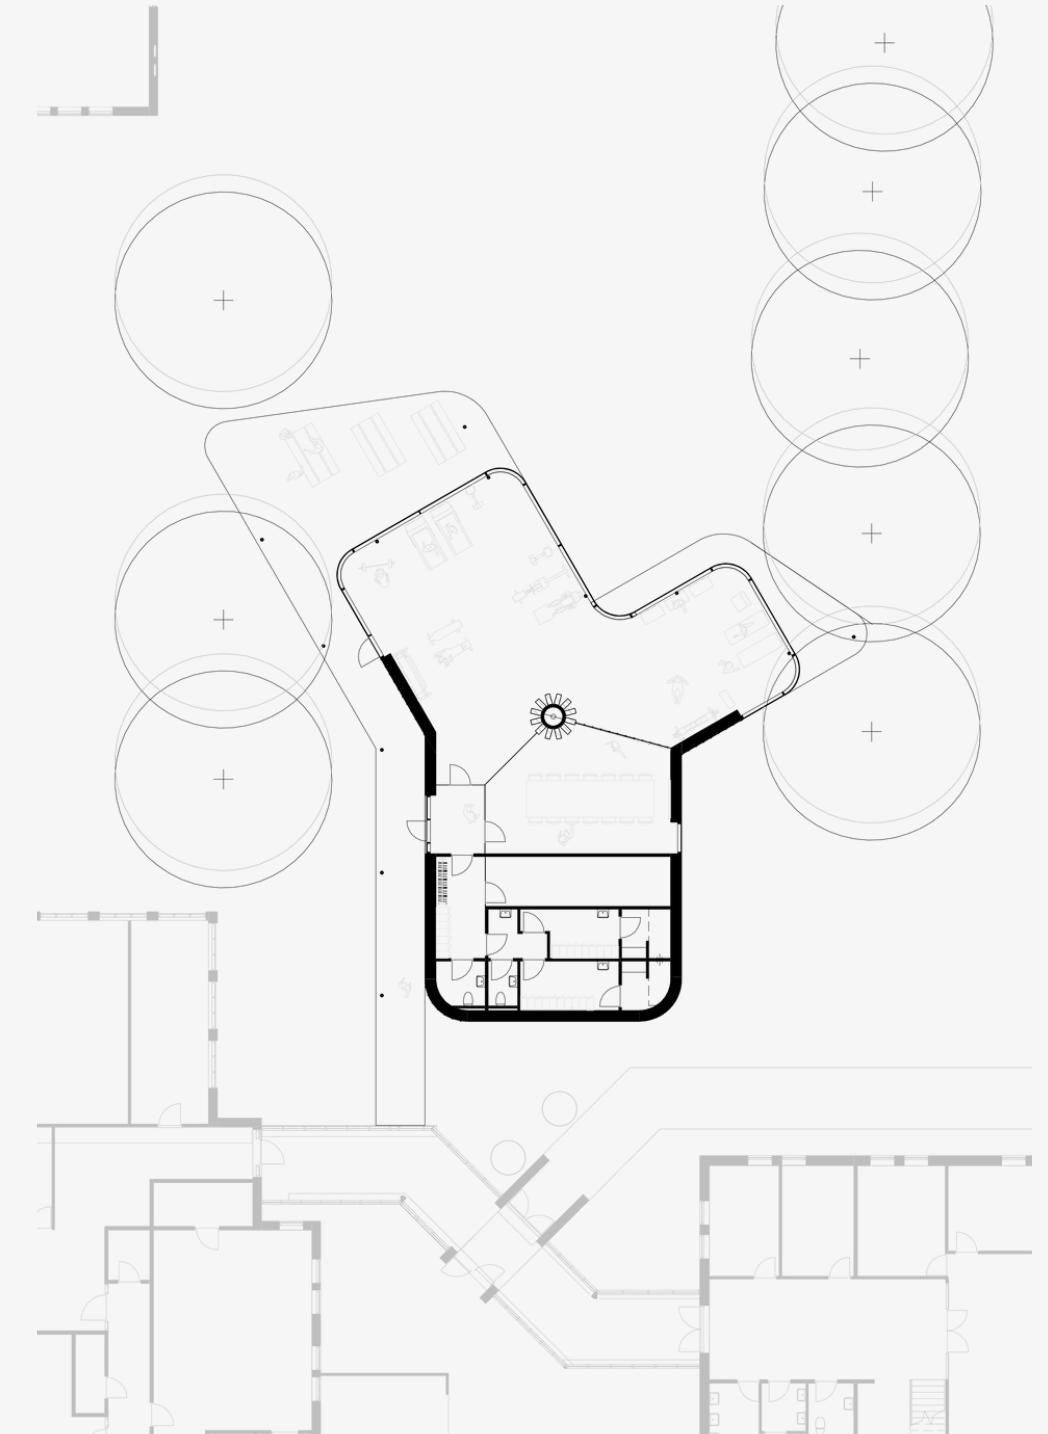

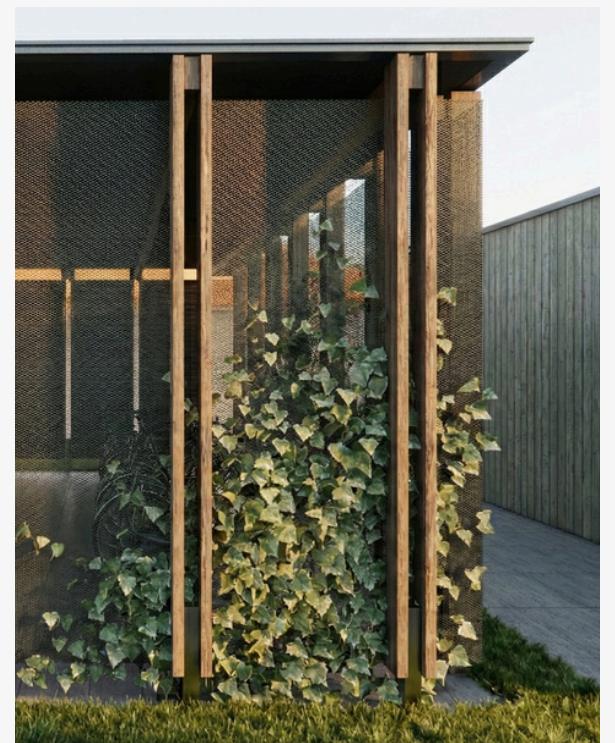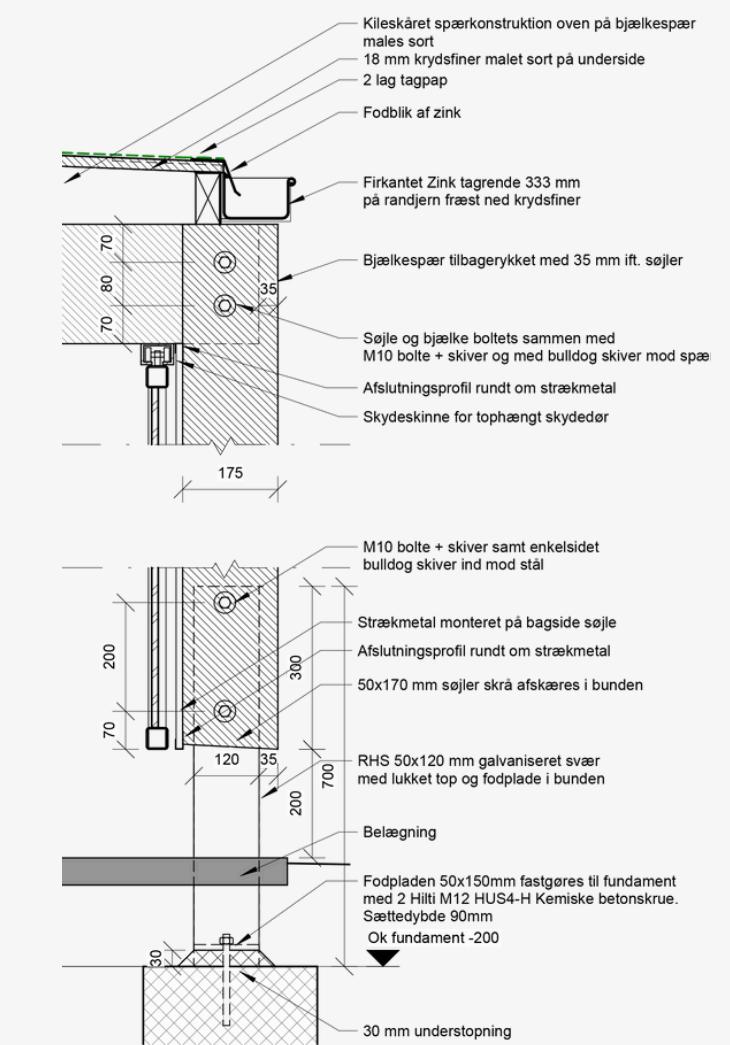

Cykelparkeringen viderefører pavillonens trælogik i en mere tilbageholdt form, hvor enkelhed, gentagelse og bygbare detaljer prioriteres. Herved gives en hverdagsfunktion samme arkitektoniske værdighed som hovedbygningen.

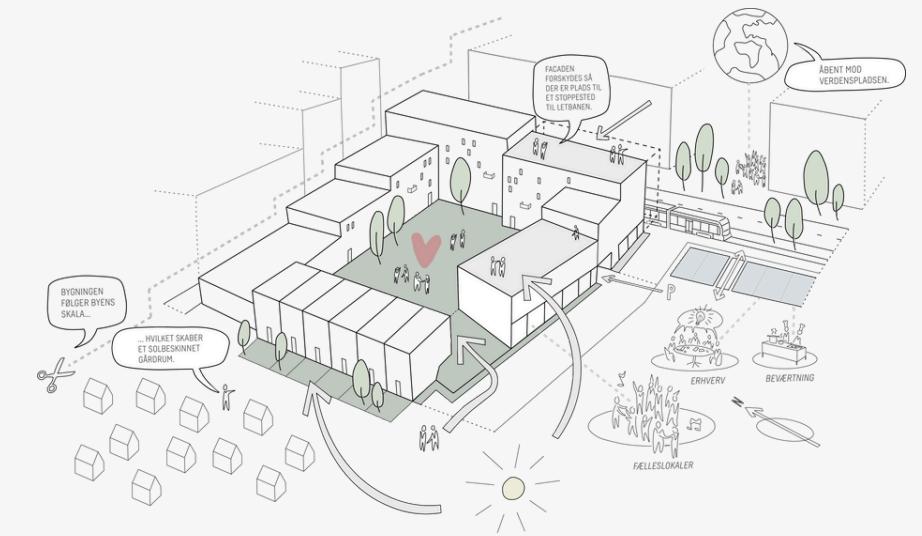

Karen Blixens Boulevard, Brabrand - Aarhus

Lokalplanområde 1208, Byomdannelse og boligkvarter – Delområde II

Projekt

Udvikling af arkitektonisk og bymæssigt oplæg for Delområde II ved Karen Blixens Boulevard i Brabrand som grundlag for lokalplan nr. 1208.


Rolle og bidrag

Udarbejdelse af det oprindelige visions- og ideoplæg samt byanalyse for Enggaard, herunder konceptuelle greb, volumetriske studier og disponering, der udgjorde beslutningsgrundlag for bygherres erhvervelse af arealet.


Efterfølgende hovedansvar for arkitektonisk bearbejdning og åbning af projektet i 1:200-skala.




Karré

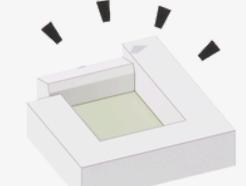


Bolig Typologier

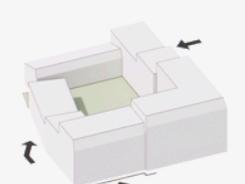


Skubning og Nedtrapning

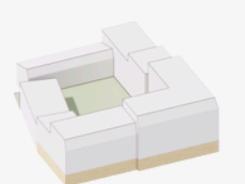

Basen - Erhverv og Butiksliv

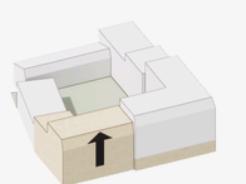

Teglbasen trækkes op

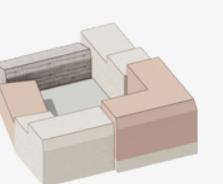

Farvetoner





Proces og samarbejde

Projektet blev udviklet gennem flerårigt samarbejde med Enggaard og Aarhus Kommune.

Det godkendte projektmateriale dannede grundlag for udarbejdelsen af lokalplan nr. 1208 ved Grandville, herunder overordnet disponering af veje, byrum og offentlige arealer, mens Vandkunsten parallelt udviklede principper for rækkehusbebyggelsen i lav skala.

Status og resultat

Lokalplan nr. 1208 blev vedtaget af Aarhus Byråd den 4. juni 2024 og offentliggjort den 20. juni 2024.

Projektet muliggjorde op til 33.000 m² bebyggelse inden for Delområde II og førte til tildeling af projektering af tre karréer samt videre arbejde med boligbebyggelser for Enggaard.



TRANSFORMATION & GENANVENDELSE

JAKA SENIORBOFÆLLESSKAB - Brabrand

Transformation / kultur / bolig
Konceptansvarlig · 2018-2026

SPARKASSEN AARUP - Aarup

Transformation / interiør
Arkitekt Lead · 2024-2025

SPX DOMICIL - Silkeborg

Transformation / erhverv
Sagsarkitekt · 2016-2017

SWECO GEOLAB – Kolding

Laboratorie / transformation
Sagsarkitekt · 2025

HOLMBOES ALLÉ 2 - Horsens

Transformation / erhverv
Sagsarkitekt / Projektleder · Idéoplæg

BYSTRUKTUR & BOLIG

KAREN BLIXENS BOULEVARD - Aarhus

ILokalplan / bolig
Projektleder / tidligfase · 2018-2025

SONNESGADE 14 – Aarhus

Bolig
Sagsarkitekt · 2018-2022

RUGÅRDSVEJ 13-15 – Odense

Lokalplan / Bolig
Sagsarkitekt / Projektleder · 2021-2023

GAMMELHAVN – Vejle

Bolig / Erhverv
Sagsarkitekt · 2021-2025

PAPIRTÅRNET – Silkeborg

Bolig
Arkitekt / Konceptansvarlig · 2016-2017

OFFENTLIGE & KULTURELLE BYGNINGER

ØSTRE SØBAD – Silkeborg

Offentligt byrum
Designansvarlig · 2017

JERN- OG METALSKOLE – Sisimiut

Offentlig uddannelse
Koncept Lead · 2025

TELEFONSMØGEN 4-4A – Aarhus

Hotel / bolig infill
Sagsarkitekt / Projektleder · 2022-2025

TECHCOLLEGE ØUV – Aalborg

Offentlig uddannelse
Arkitekt Lead · Dispositionsforslag · 2024

DANSK TRAILCENTER – Silkeborg

Offentlig fritid
Designansvarlig · 2017

NY STADION I AARHUS - Aarhus

Idræt
Analyse / koordinering · 2022

ERHVERV & INDUSTRI

- KK WINDSOLUTIONS FITNESS PAVILLON – Ikast
KK WINDSOLUTIONS ELEKTRONIKOMRÅDE – Ikast
GMB LILLEHØJVEJ – Silkeborg
CO-RO INNOVATORIUM (KON) – Frederikssund
LEO PHARMA NYT DOMICIL (KON) – Ballerup
NETTO, SILKEBORGVEJ – Aarhus
- Erhverv / fritid · Sagsarkitekt / Projektleder · 2024-
Transformation / erhverv · Sagsarkitekt / Projektleder · 2024-
Helhedsplan / erhverv (træbyggeri) · Kreativleder / Skitserende · 2024
Erhverv · Skitserende · 2016
Erhverv · Arkitekt Lead · 2019
Detailhandel / facade · Sagsarkitekt · 2021 (Aarhus Kommune Særpris 2022)

**STUDIER, TIDLIGFASE &
STRATEGISKE KONCEPTER**

- SKAGEN MILE / LILLE SKAGEN MULTICENTER – Skagen
LYSTRUP BYMIDTE UDVIKLING – Lystrup
STRØGCENTER IKAST – VISIONSKATALOG – Ikast
HOLSTEBRO HØJHUS – VISIONSPLAN – Holstebro
DET GRØNNE RUM – Durup
GØDVAD KIRKEVEJ STRUKTURPLAN – Silkeborg
SKIVEVEJ HOLST / HOLSTEBRO VISIONSPLAN – Holstebro
- Rekreativ / oplevelse · Skitserende / Konceptudvikling · 2023
Helhedsplan / Kultur / Bolig · Sagsarkitekt · 2022-
Helhedsplan / vision · Sagsarkitekt / Projektleder · 2024-
Hotel / mixed use · Arkitekt Lead · 2024-
Kultur / Genbrug · Skitserende / Konceptudvikling · 2024-
Helhedsplan / struktur · Skitserende · 2021
Helhedsplan / bolig · Skitserende · 2019

Udvalg af projekter. Fuldt projekt-CV omfatter 80+ projekter. Udvidet projekt-CV og supplerende materiale fremsendes gerne.